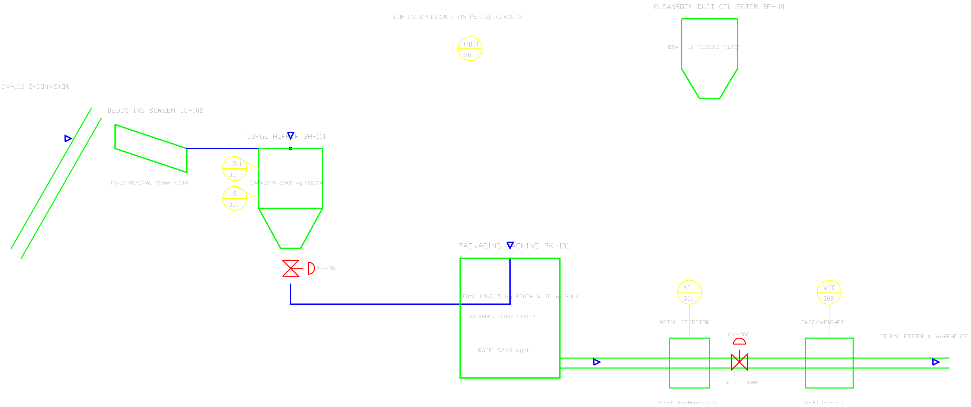

PACKAGING HACCP CRITICAL CONTROL POINTS (CCP-1 & CCP-2):

1. CCP-1 (Metal Detection): MD-301 tested every 2h with test wands (1.5mm Fe, 2.0mm Non-Fe, 2.5mm SS).
2. Any metal detection immediately triggers pneumatic reject flap XV-302 and alarms packaging operator.
3. CCP-2 (Moisture Verification): Final packaged product moisture locked @ 10.0% +/- 0.5% wet-basis.
4. Nitrogen Gas Flush: Residual headspace oxygen < 2.0% to guarantee 12-month shelf life without oxidation.
5. ISO Class 8 Cleanroom: Differential pressure > +15 Pa maintained against raw warehouse to prevent cross-contamination.

CONCEPTUAL FEED - PRELIMINARY - NOT FOR CONSTRUCTION / NOT FOR PROCUREMENT

HARAKUTIR AGRO-PROCESS ENGINEERING PVT. LTD.
15,000 kg/day Split Pigeon Pea Optimization Greenfield Project

P&ID - PACKAGING LINE & CLEANROOM DEDUSTING
DISCIPLINE: PIPING | STAGE: CONCEPTUAL FEED

DWG NO: DWG-FIN-15T-006	REV: V4.0	SHEET: 6 OF 12
SCALE: AS SHOWN DATE: 2026-10-15	STATUS: PRELIMINARY	GATE: G-A HOLD